
MP SHOOT — FLOOR 4

CRIME READER DIVISION / ARCHITECTURAL PLAN 01

DESIGN REVIEW · PLAN ONLY · REV 01

A3 LANDSCAPE / 1:250 AT ORIGINAL PRINT SIZE

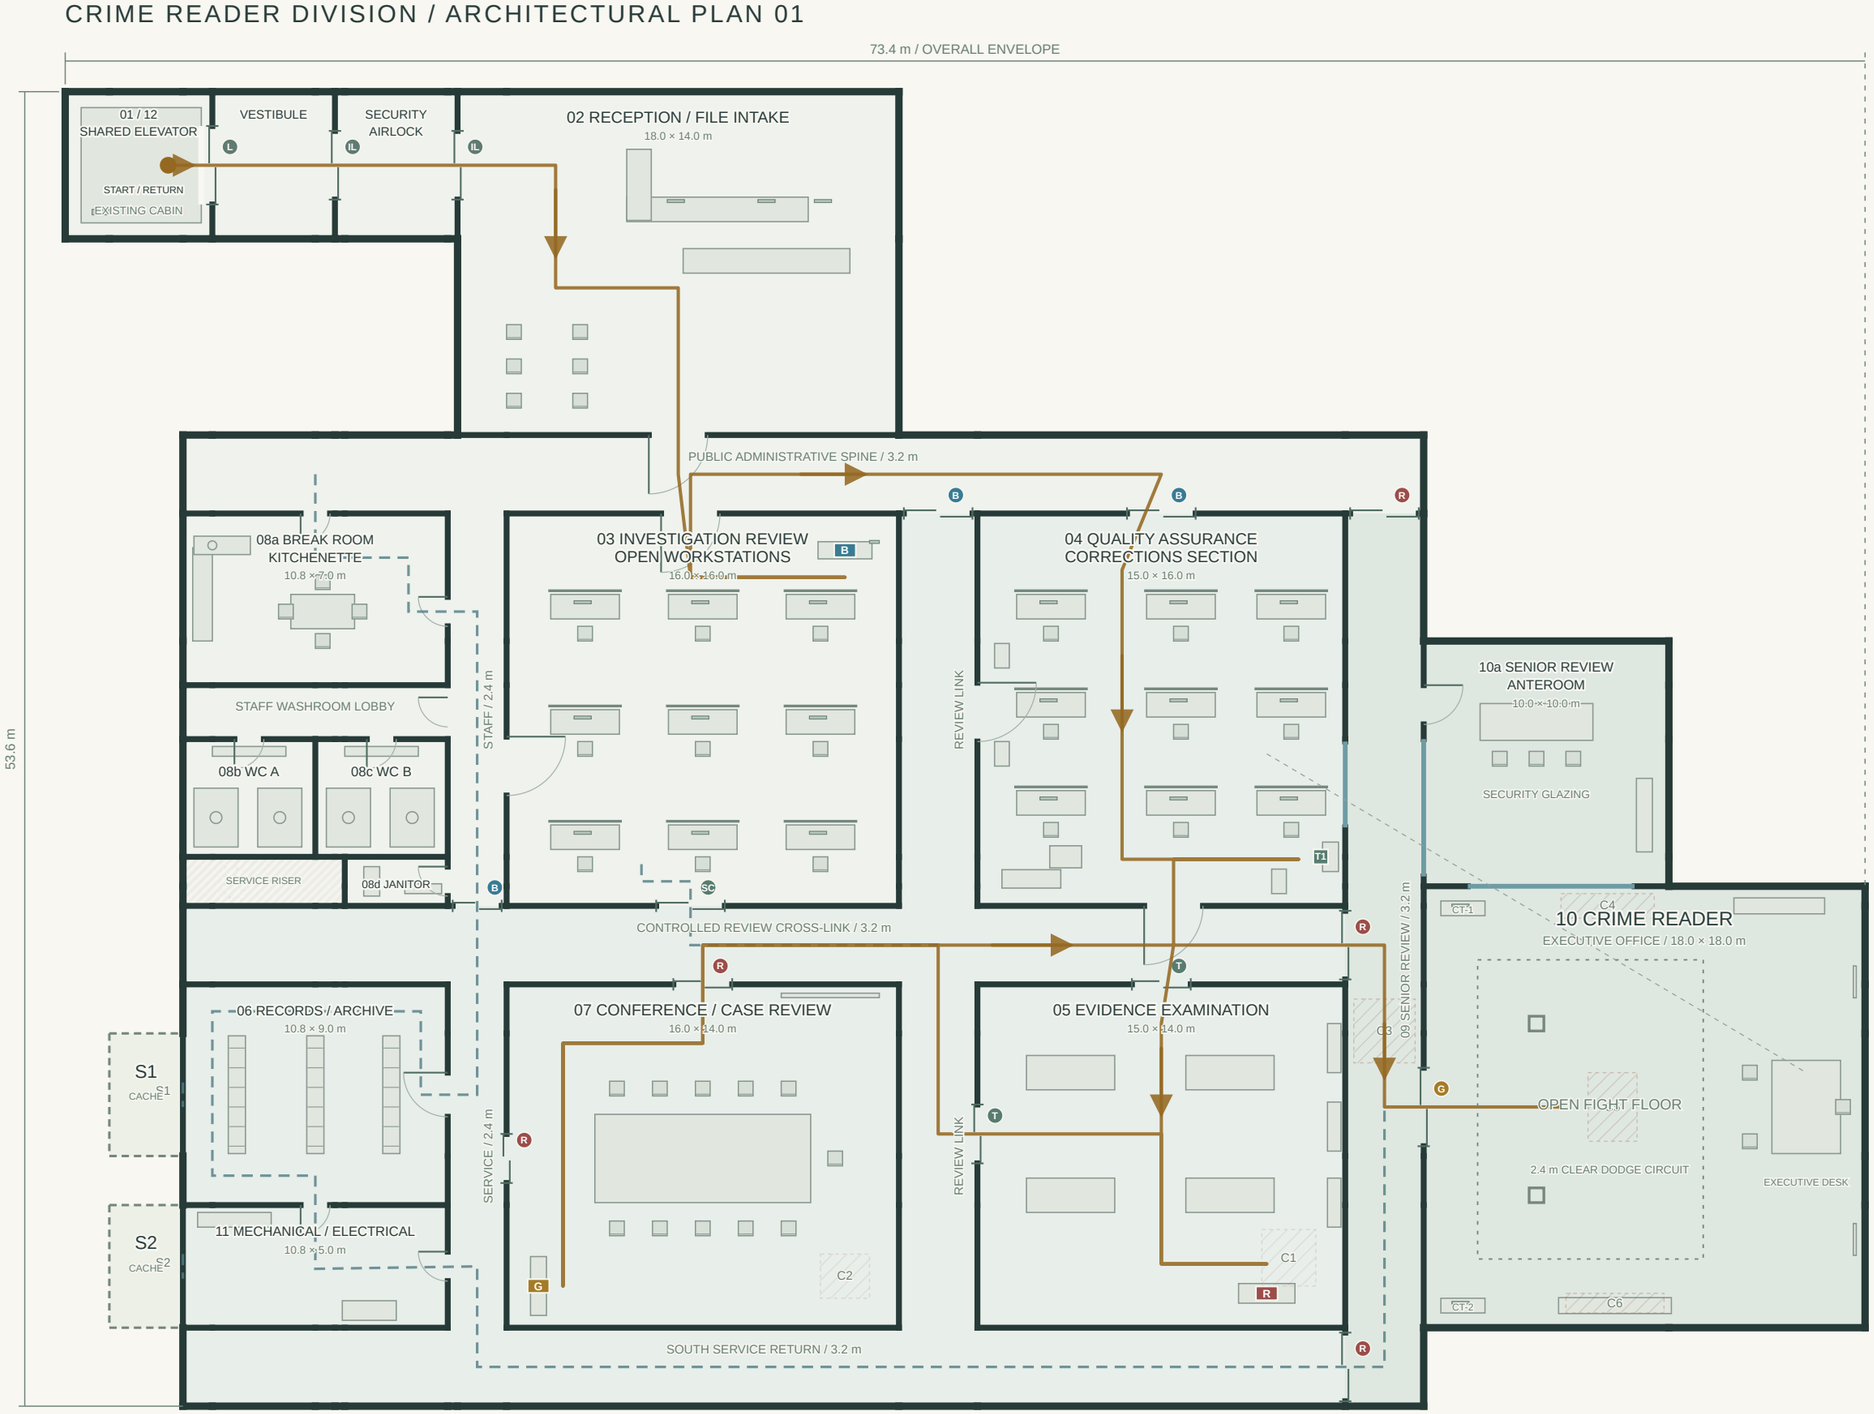

ACCESS & DRAWING KEY

- B — Blue / controlled review access
- R — Red / senior + case-review access
- G — Gold / boss entrance only
- T — T1 release / evidence doors
- SC — SC1 / return shortcut after T1

Solid ochre: suggested primary route
Dashed teal: secondary / service routes
Blue dash: post-boss return (toggle)
Paired leaves: controlled sliding door
Arc: ordinary door swing indication
Glazing: view only / no bypass
S1 / S2: optional concealed caches

PRIMARY PROGRESSION

01 → 02 → 03: recover BLUE access
04: route corrections at terminal T1
T1 opens evidence + shortcut SC1
05: recover RED review access
07: recover GOLD boss authorization
09 → 10: enter the Crime Reader office
After boss: release the SAME elevator
12: return to cabin / descend to Floor 5

CORRUPTION / FUTURE WORK

First half: conventional office finishes
C1–C2: sparse, subtle late-file anomalies
C3: first visible senior-suite fissure
C4–C6: boss transformation positions
CT-1 / CT-2: correction-terminal bays
Hatching is a reservation, not a hazard
Keep the marked dodge circuit clear

ELEVATOR & SCALE

One 6 × 6 m elevator envelope
Same model / east-facing arrival
Plan origin = world (−44, −39)
Spawn = (−39.8, −36), facing east
Wall centres shown; wall t = 0.24 m
Main circulation 3.2 m / service 2.4 m
Room dimensions are to wall centres

REQUIRED ROOM SCHEDULE

01 / 12 One shared elevator + vestibule / airlock
02 Reception / File Intake
03 Investigation Review Office
04 Quality Assurance / Corrections
05 Evidence Examination
06 Compact Records / Archive
07 Conference / Case Review
08 Break room, washrooms + janitor
09 Senior Review Corridor
10 Crime Reader office + anteroom
11 Mechanical / Electrical
S1 / S2 Optional concealed caches

Envelope: 73.4 × 53.6 m · Enclosed layout: 2,806 m² incl. circulation / service riser · Irregular perimeter

First architectural draft only. Existing Floors 1–3 remain unchanged. Boss mechanics / corruption effects are future implementation work.

0 5 10 m